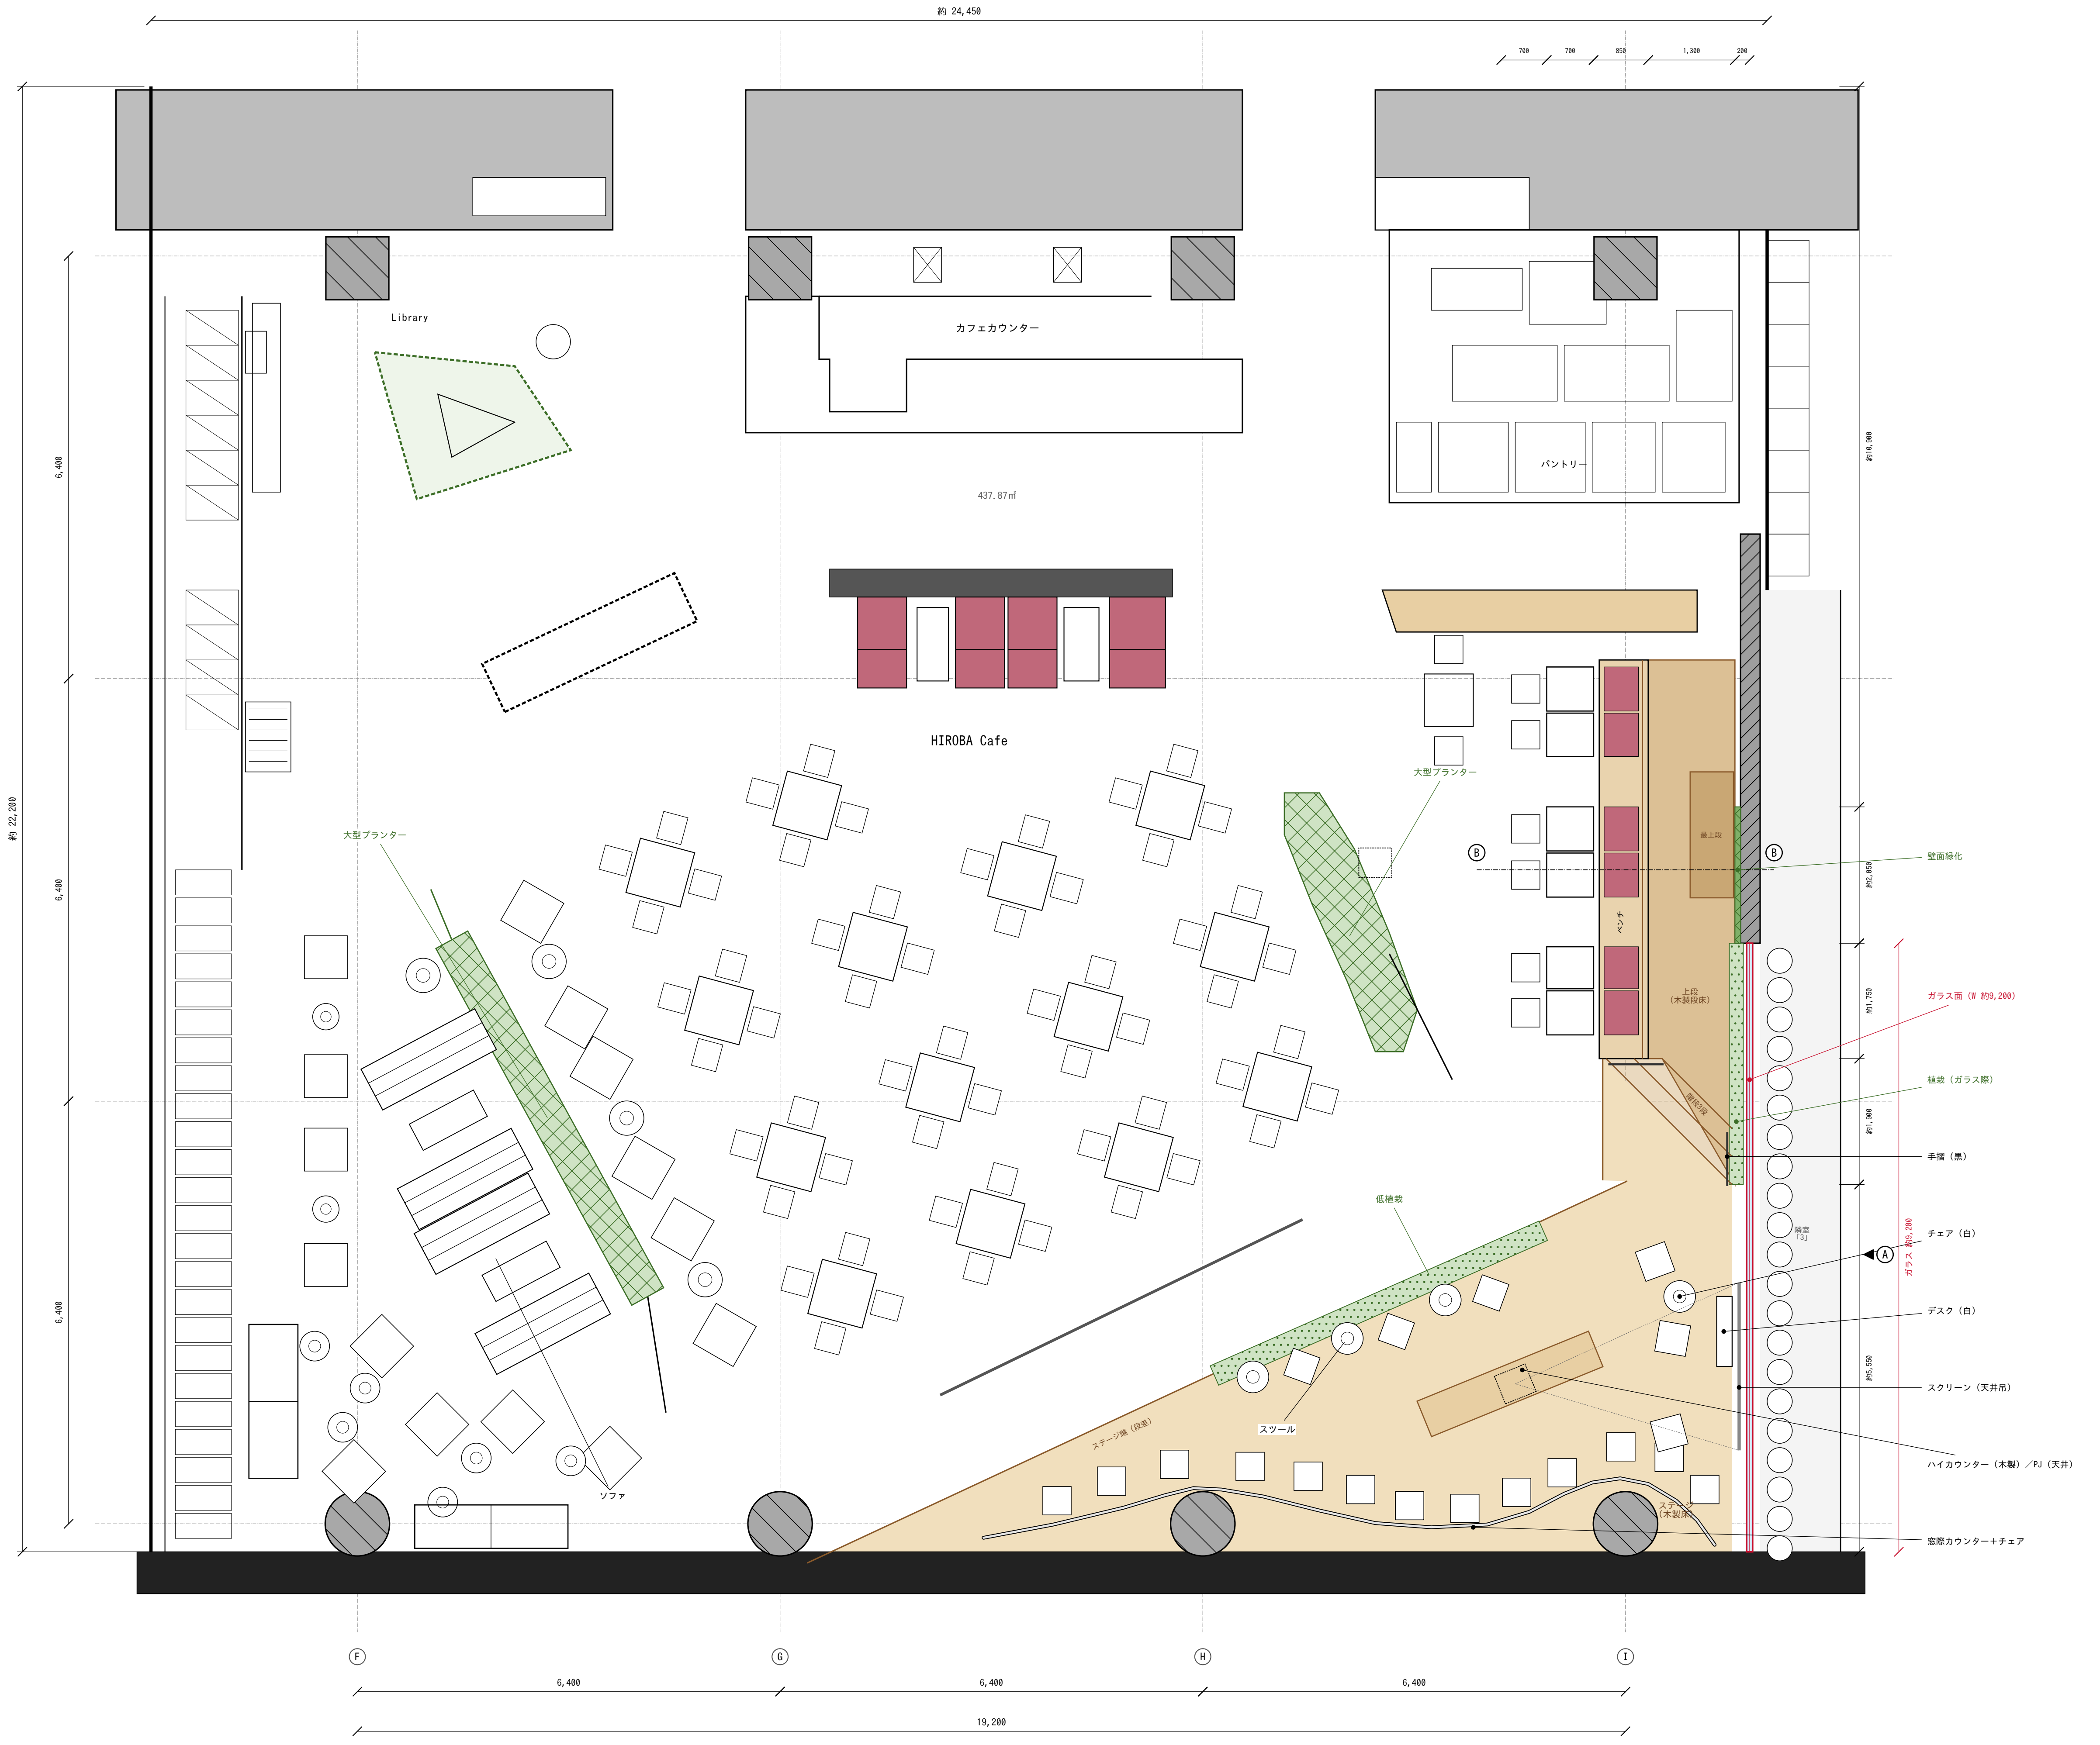

# HIROBA 平面図
# （完全版）S=1/100

通り芯 6,400（F～I 19,200）を
基準に縮尺確定。
右下部分は現況写真と照合。

図上北

凡例

| | |
|---|---|
| 🟧 | ステージ（木製床） |
| 🟫 | 木製段床 |
| 🟥 | ベンチ座面 |
| ▨ | 植栽 |
| 🟩 | 壁面緑化 |
| 🟦 | ガラス面 |
| ▨ | 柱 |
| ☐ | 天井設置（PJ） |
| - - - | 通り芯 |

SCALE 1/100 (A3)

0 1 2 3 4 5m

| | |
|---|---|
| 図面名 | HIROBA 平面図（完全版） |
| 縮尺 | 1/100（A3） |
| 日付/番号 | 2026.10.15　1/2 |

## A 展開図（ガラス面・西より見る）　S=1/100

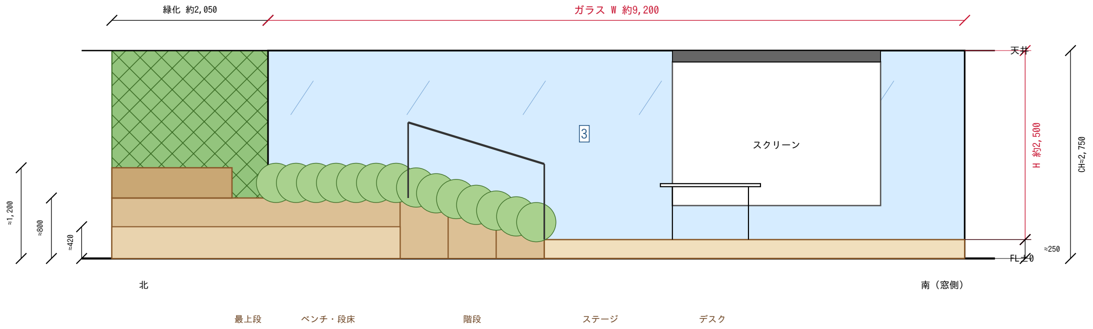

参考：現況写真（A面 北西より）

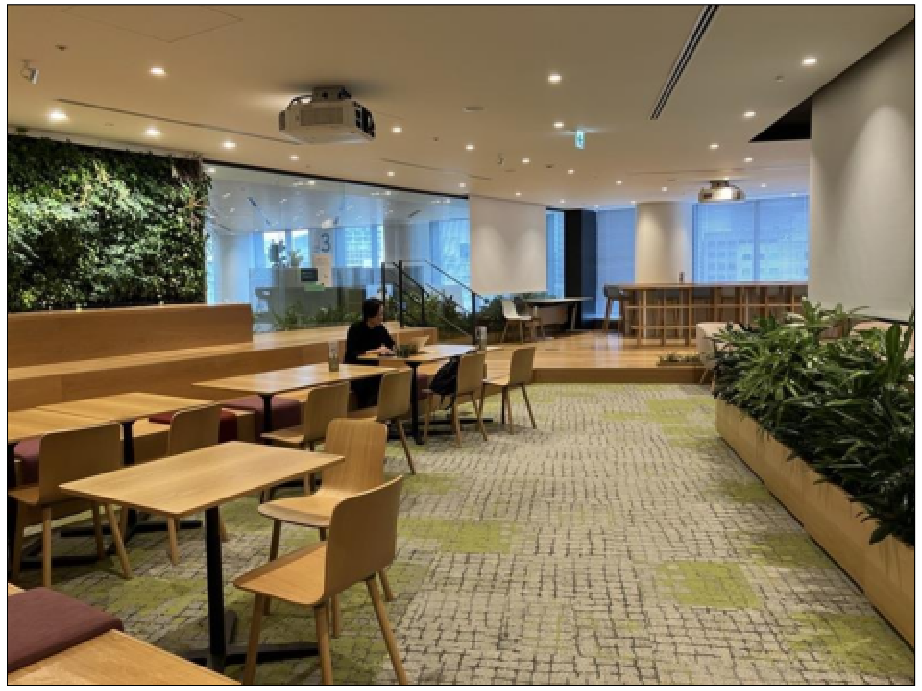

## B-B 断面（ベンチ・段床）　S=1/100

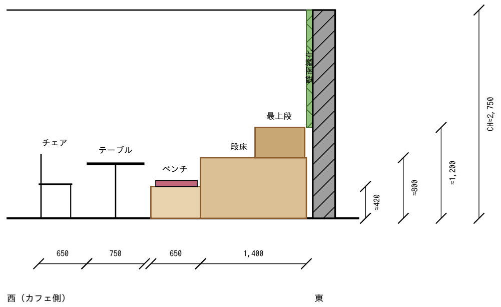

【作図根拠・注記】

1. 元図面（HIROBA図）をトレース。縮尺は正式図面の通り芯 6,400（F～I 19,200）で確定。

   （≒105.9mm/px）。ガラス面は約9,200（指示値 約9m と整合）。

2. 右下部分は現況写真（ブース北西→南東方向）と照合して詳細化：

   壁面緑化／赤クッションのベンチ＋木製段床／黒手摺付き階段3段／

   木製ステージ（白チェア・白デスク）／天井吊スクリーン・PJ／木製ハイカウンター

3. ガラス W約9,200 は緑化端～南端（スクリーン背面を含む）。

4. 高さ（≈表記）は写真の透視からの推定値。H2,500 はステージ床からの値。

5. 平面寸法の誤差：通り芯基準で ±100～200mm 程度。家具位置は実測で要確認。

6. 家具配置は正式図面（高解像度）と照合して修正済み。

SCALE 1/100 (A3)

| | |
|---|---|
| 図面名 | A展開図・B-B断面 |
| 縮尺 | 1/100 (A3) |
| 日付/番号 | 2026.10.15　2/2 |