
HIROBA 平面図（完全版）　S=1/100

元図面トレース＋右下部分は現況写真と照合して詳細化

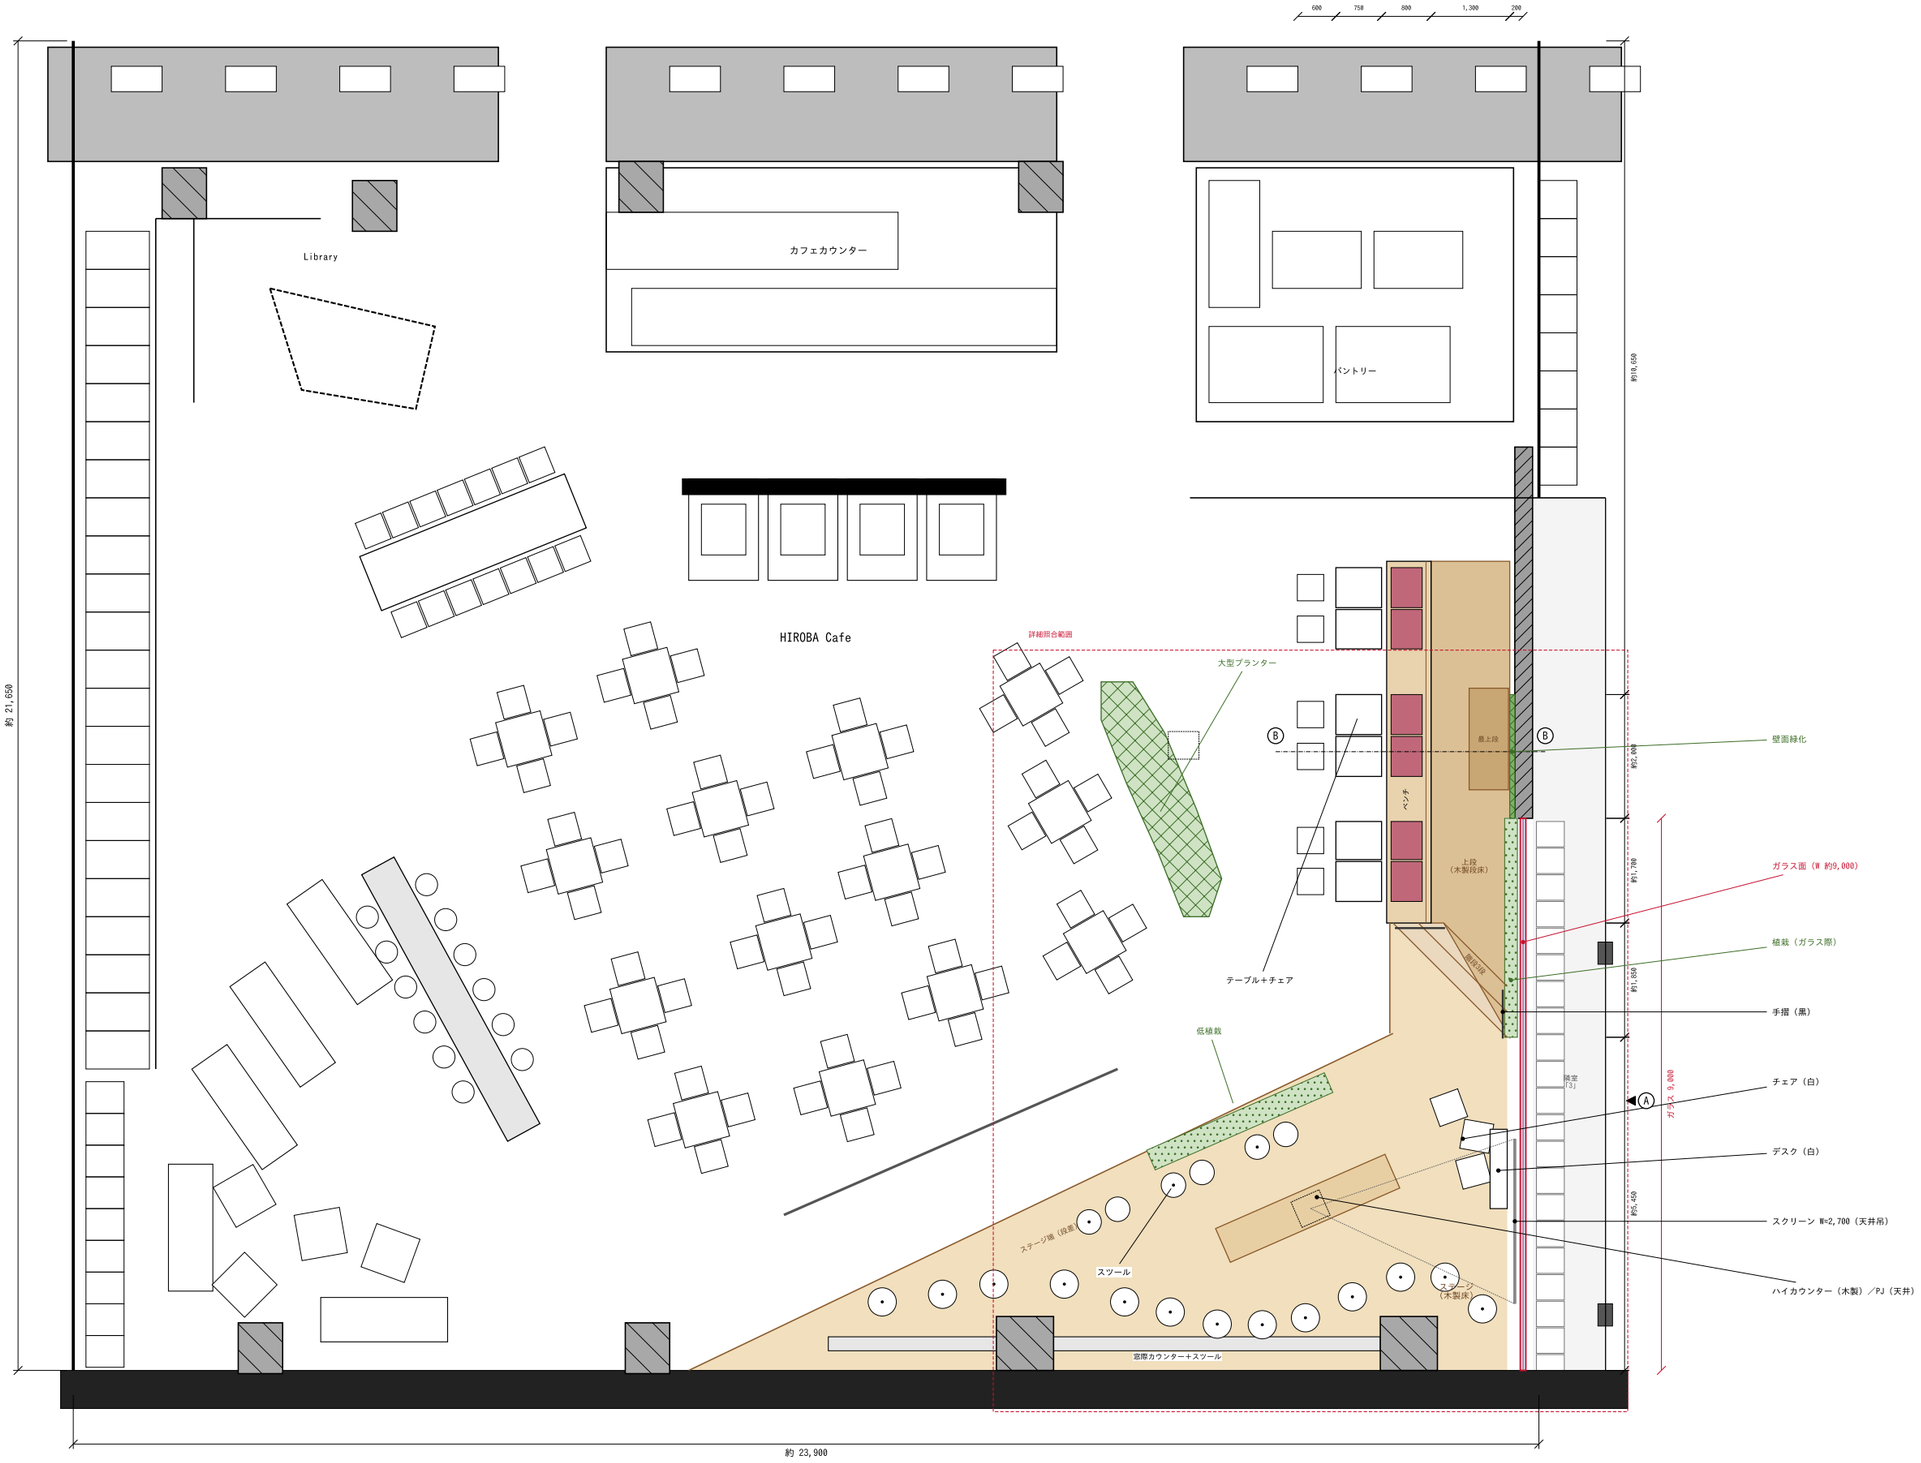

図上北

凡例


- ステージ（木製床）
- 木製段床
- ベンチクッション
- 植栽
- 壁面緑化
- ガラス面
- 柱
- 天井設置（PJ）

SCALE 1/100 (A3)


0　1　2　3　4　5m

図面名	HIROBA 平面図（完全版）
縮尺	1/100（A3）
日付/番号	2026.10.13　1/2

A 展開図（ガラス面・西より見る）　S=1/100

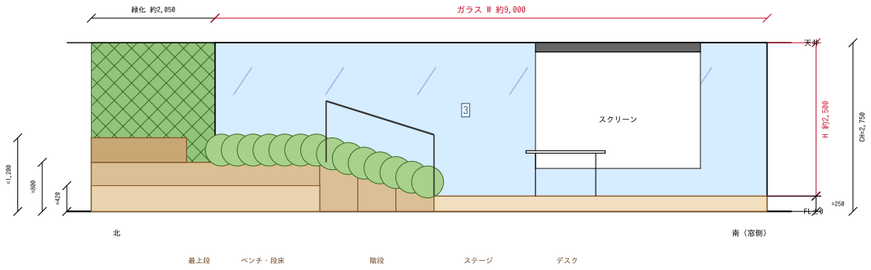

B-B 断面（ベンチ・段床）　S=1/100

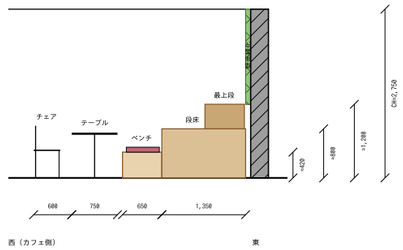

参考：現況写真（A面 北西より）



【作図根拠・注記】

1. 元図面（HIROBA図）をトレース。縮尺はガラス面 87px＝9,000mm（≒103mm/px）で換算。
   テーブル700・椅子450・段板=290 と整合を確認済み。
2. 右下部分は現況写真（ブース北西→南東方向）と照合して詳細化：
   壁面緑化／赤クッションのベンチ＋木製段床／黒手摺付き階段3段／
   木製ステージ（白チェア・白デスク）／天井吊スクリーン・PJ／木製ハイカウンター
3. ガラス W9,000 は緑化端〜南端（スクリーン背面を含む）。
4. 高さ（=表記）は写真の透視からの推定値。H2,500 はステージ床からの値。
5. 平面寸法の誤差：右下 ±100〜200mm、その他 ±300mm 程度。実測で要確認。
6. 右下以外の家具配置は元図面の概略トレース。

SCALE 1/100 (A3)



図面名	A展開図・B-B断面
縮尺	1/100 (A3)
日付/番号	2026.10.13　2/2