


HIROBA 右下部分 詳細平面図　S=1/100

元図面トレース＋現況写真照合（ガラス面 W9,000 を基準に縮尺換算）

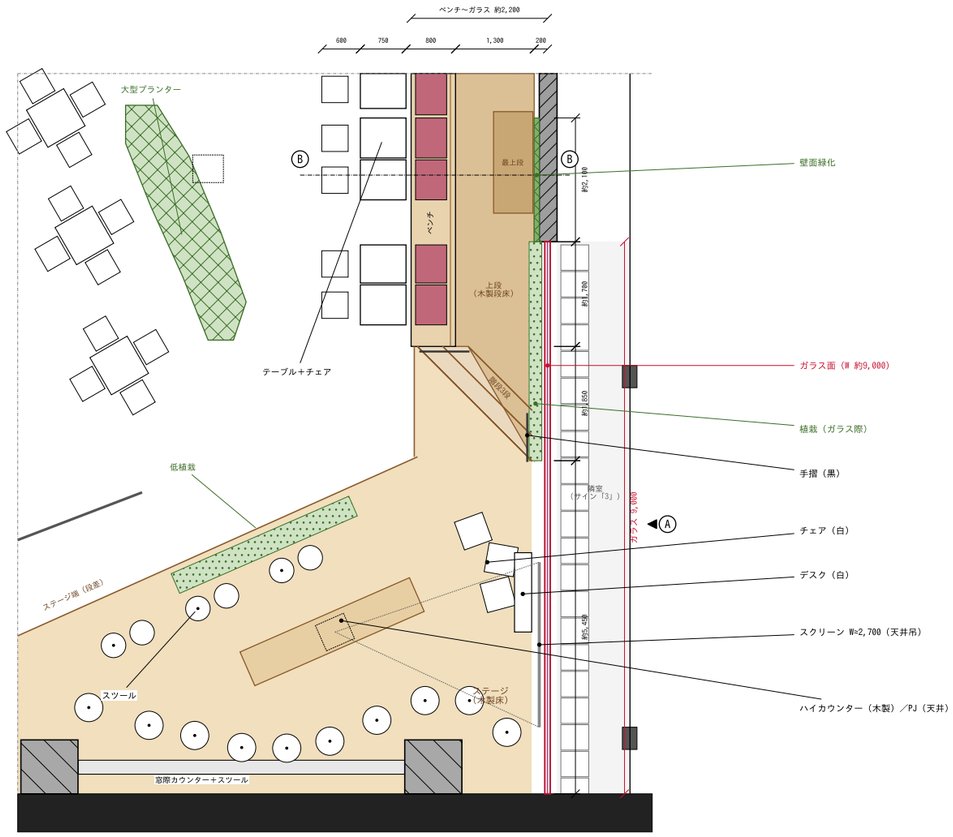


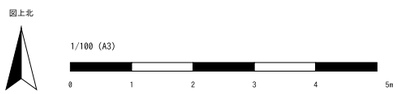

A 展開図（ガラス面・西より見る）　S=1/100

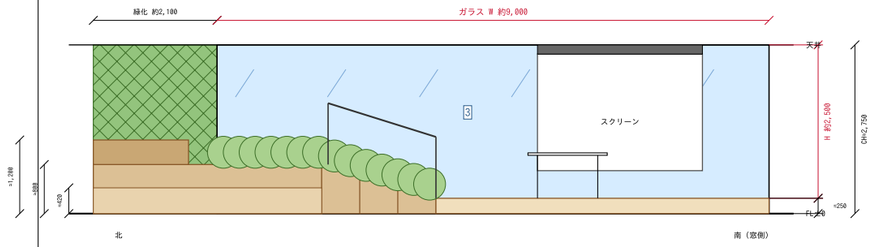

B-B 断面（ベンチ・段床）　S=1/100

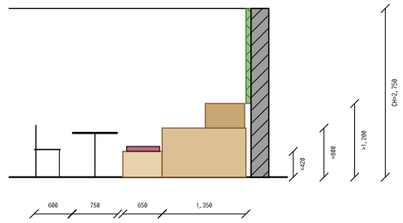

キープラン（元図面）



【作図根拠・注記】

1. 平面は元図面（HIROBA図）を画素単位でトレース。縮尺はガラス面 87px＝9,000mm（≒103mm/px）で換算。テーブル700・椅子450・段板≈290 と整合を確認済み。
2. 写真は本図ブース北西から南東方向を撮影したものと判断し、以下を照合：
   - 壁面緑化（ガラス北端）・赤クッションのベンチ＋木製段床・黒手摺付き階段
   - 木製ステージ（白チェア・白デスク）・天井吊スクリーン・PJ・木製ハイカウンター
3. ガラス W9,000 は緑化端～南端。写真の矢印終点はスクリーンで隠れる手前まで。
4. 高さ（=表記）は写真の透視からの推定値。H2,500 はステージ床からの値。
5. 平面寸法の誤差は元図面解像度により ±100～200mm 程度。実測で要確認。

図面名	HIROBA 右下部分 詳細
縮尺	1/100 (A3)
日付	2026.10.13