


A 展開図（ガラス面・西より見る）　S=1/100

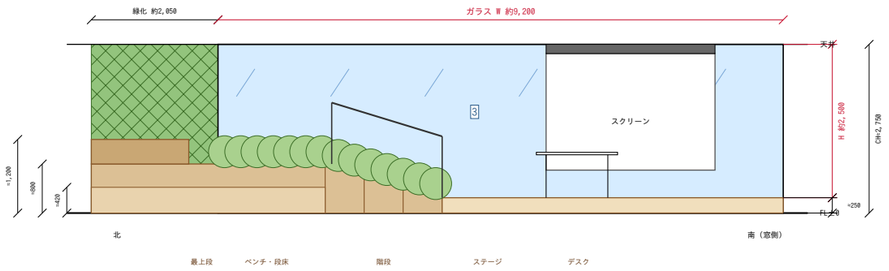

C 展開図（窓面・北より見る）　S=1/100

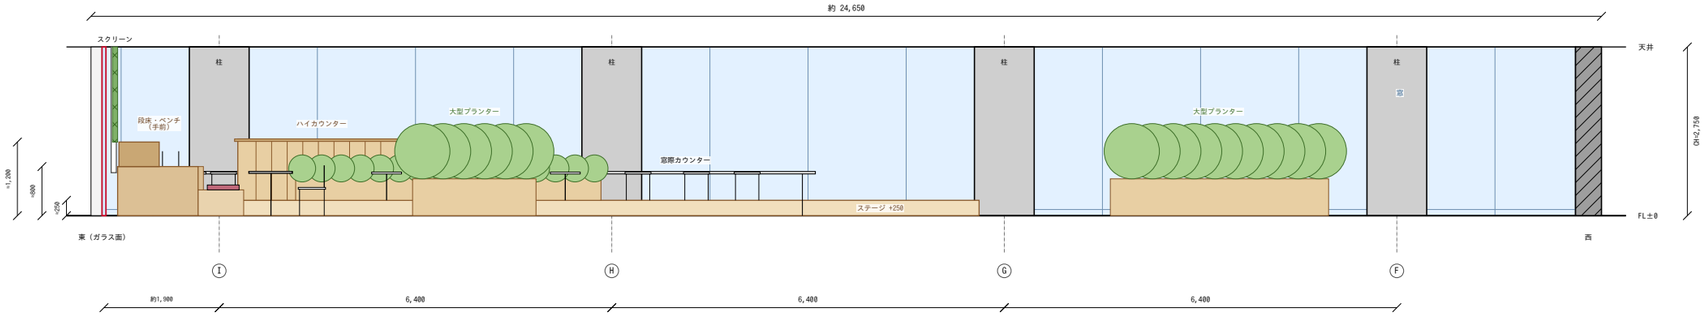

キープラン（視点方向）

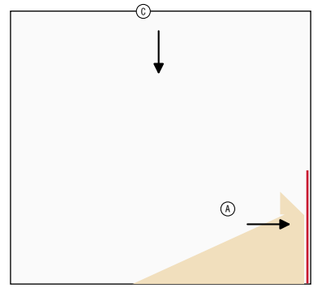

【注記】

1. 通り芯 6,400（F〜I）基準。平面位置は完全版平面図 v2 と同一データ。
2. 高さ（=表記）は現況写真からの推定値。実測で要確認。
3. C展開図の窓マリオン割付（1,600）・窓台高さは推定。
4. C展開図は主要な造作・家具のみ表示（カフェテーブル等は省略）。
5. ガラス面 W約9,200（緑化端〜南端）。H2,500 はステージ床から。

SCALE 1/100 (A3)

0　1　2　3　4　5m

図面名	A・C 展開図
縮尺	1/100 (A3)
日付/番号	2026.10.15　1/1