

HIROBA 平面図　S=1/100

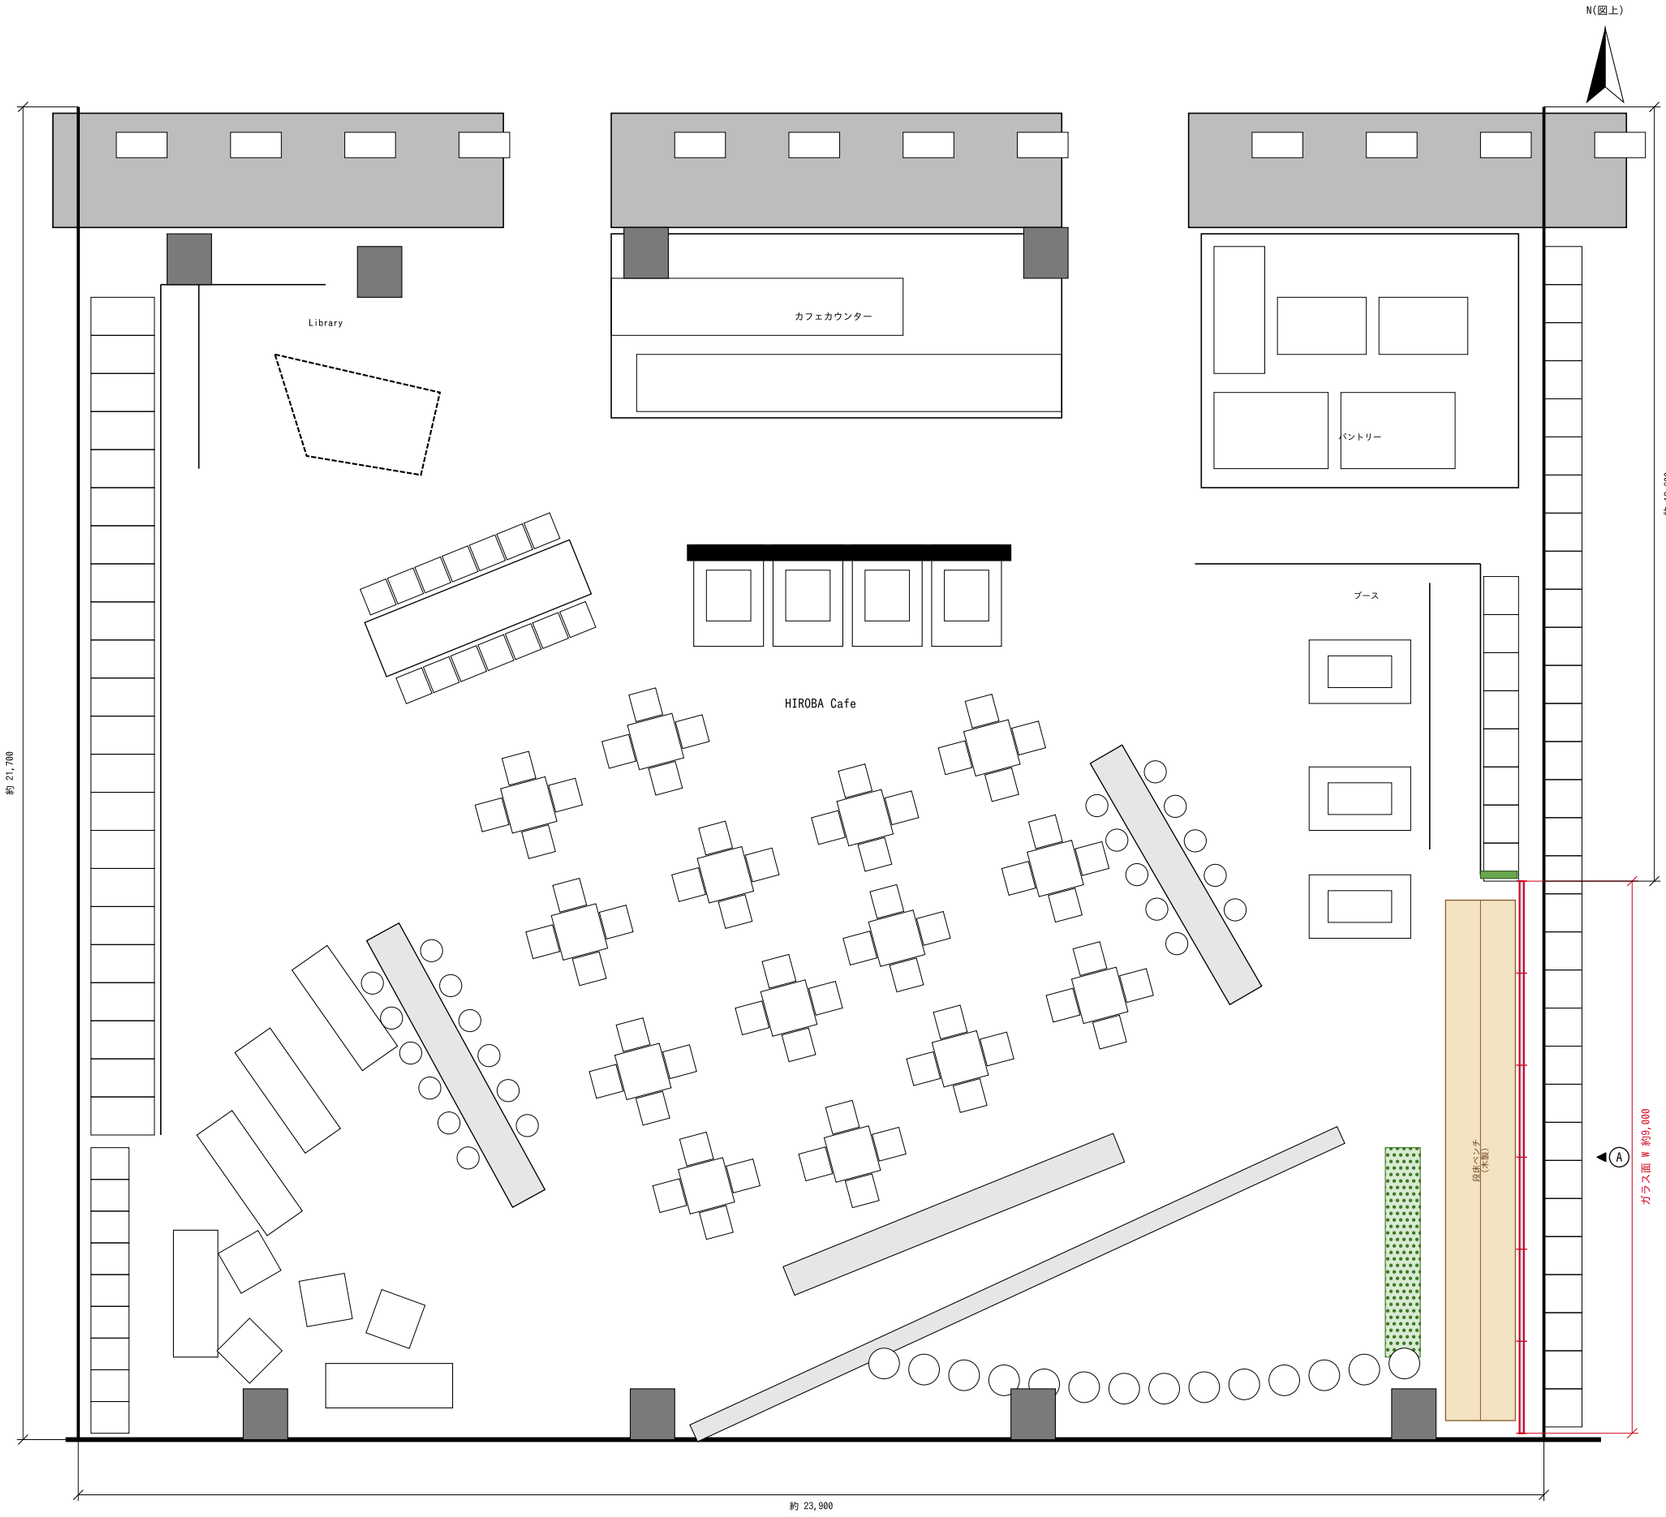

A 展開図（ガラス面）　S=1/100

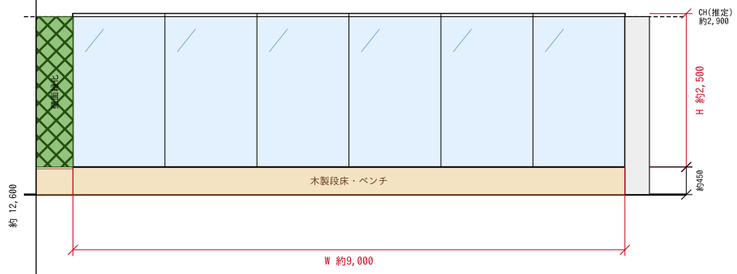

【作図条件】

1. 縮尺はガラス面幅 約9,000mm（写真・指示値）を基準に元図面から換算。
   元図面の解像度上、各寸法の誤差は ±300mm 程度を想定。
2. 家具・什器位置は元図面のトレース（概略）。実測で要確認。
3. ガラス面高さ 約2,500mm は木製段床上端からの寸法（写真の矢印位置）。
4. 段床高さ・天井高・マリオン割付（6分割）・壁面緑化位置は写真から推定。
5. A3 横で出力時に S=1/100。

SCALE 1/100 (A3)

0　1　2　3　4　5m

図面名	HIROBA 平面図・A展開図
縮尺	1/100 (A3)
日付	2026.10.13